




7 A6.0 NORTH WALL SIGNAGE
1/2" = 1'-0"

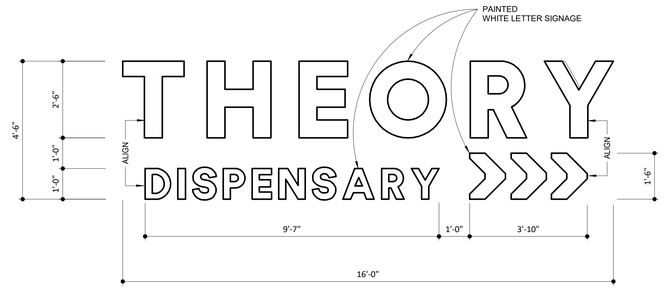


6 A6.0 EAST WALL SIGNAGE
1/2" = 1'-0"

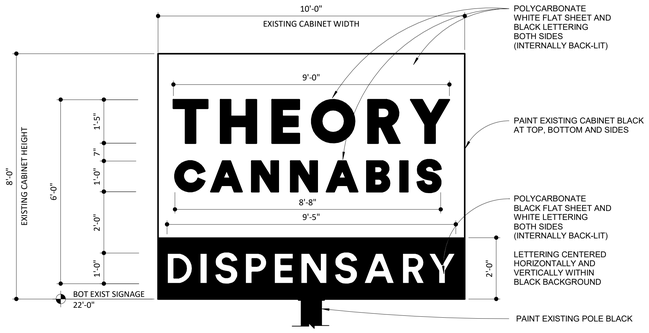


5 A6.0 EXTERIOR FREE STANDING SIGNAGE ON EXISTING POST
1/2" = 1'-0"

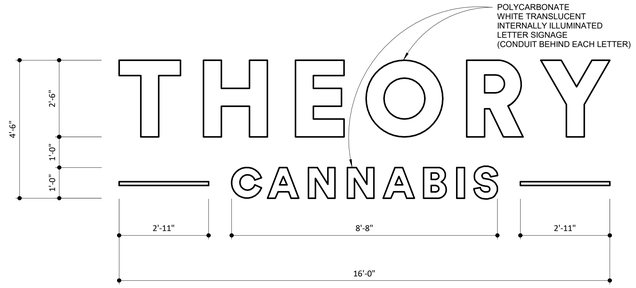

4 A6.0 SOUTH WALL SIGNAGE
1/2" = 1'-0"

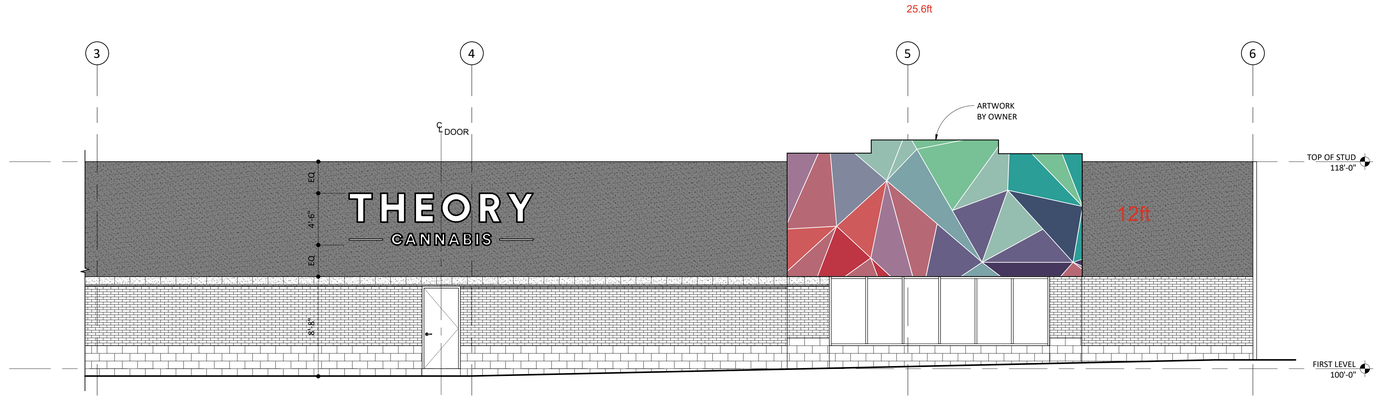


3 A6.0 SOUTH ELEVATION (SOUTH SIGNAGE)
3/16" = 1'-0"

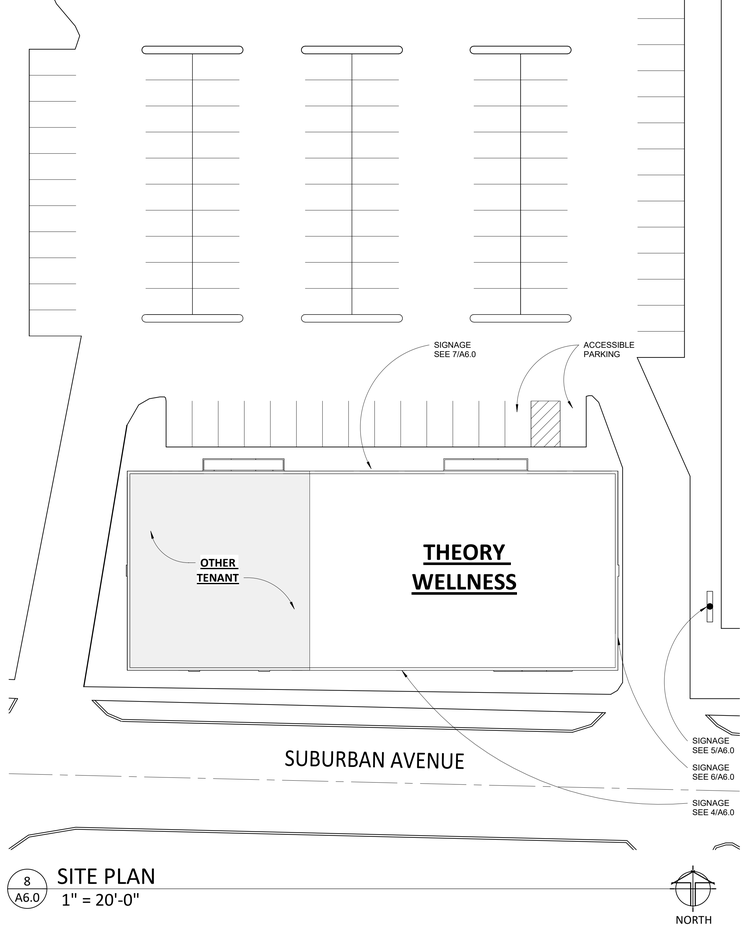

8 A6.0 SITE PLAN
1" = 20'-0"



2 A6.0 NORTH ELEVATION (NORTH SIGNAGE)
3/16" = 1'-0"

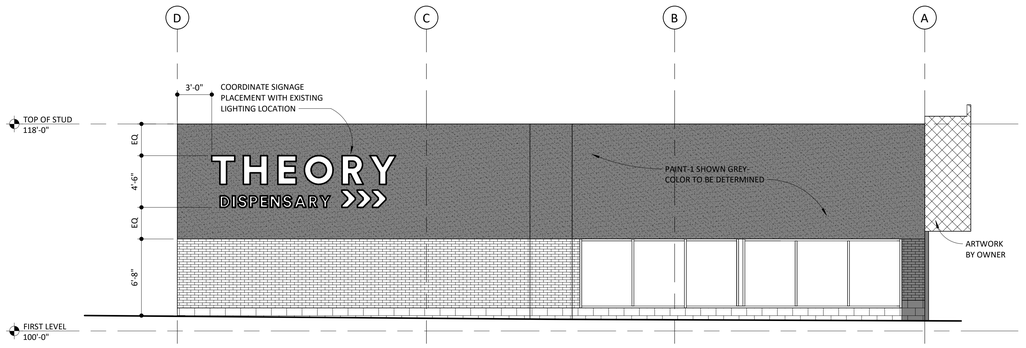

1 A6.0 EAST ELEVATION (EAST SIGNAGE)
3/16" = 1'-0"

pope DESIGN GROUP

POPE DESIGN GROUP
767 N. EUSTIS STREET, SUITE 190
ST. PAUL, MINNESOTA 55114
651.642.9200
WWW.POPEDESIGN.COM

THEORY
WELLNESS

THEORY
WELLNESS
TENANT
IMPROVEMENT
1907 SUBURBAN AVENUE
ST. PAUL, MINNESOTA 55119

EXTERIOR SIGNAGE ELEVATIONS AND DETAILS

ISSUES & REVISIONS		DATE
1	SIGNAGE PERMIT	11-12-25

I hereby certify that this plan, specification, or report was prepared by me or under my direct supervision and that I am a duly Licensed Architect under the laws of the State of Minnesota

Name of Signing Architect
Date: 11-14-2025 Lic No: 51570

COMMISSION NO: 73256-25102
DRAWN BY: JJW
CHECKED BY: JJW

SHEET

A6.0

TRUE SHEET SCALE
0" 1/2" 1"

Autodesk Docs://73256-25102 Theory Wellness - St. Paul TI/73256-25125_TheoryWellness-StPaul-TI_R23.rvt
11/12/2025 3:25:03 PM