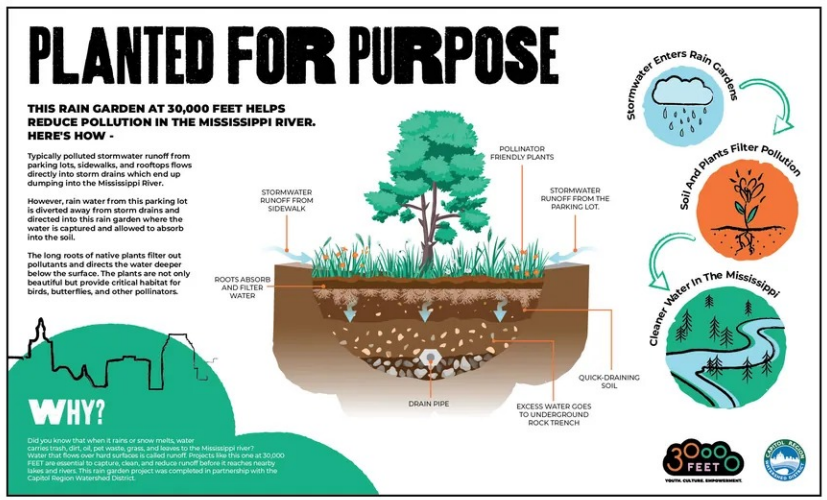
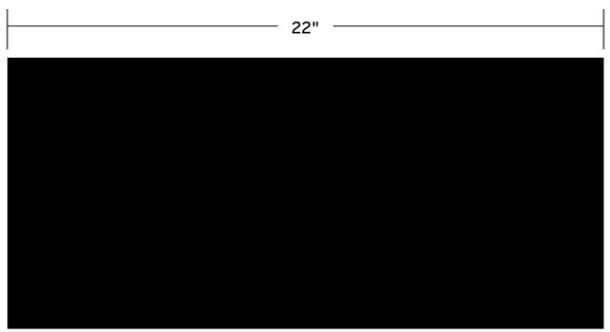


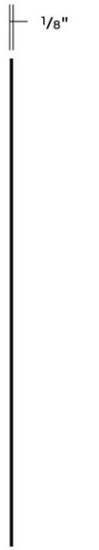

MAXMETAL PANEL



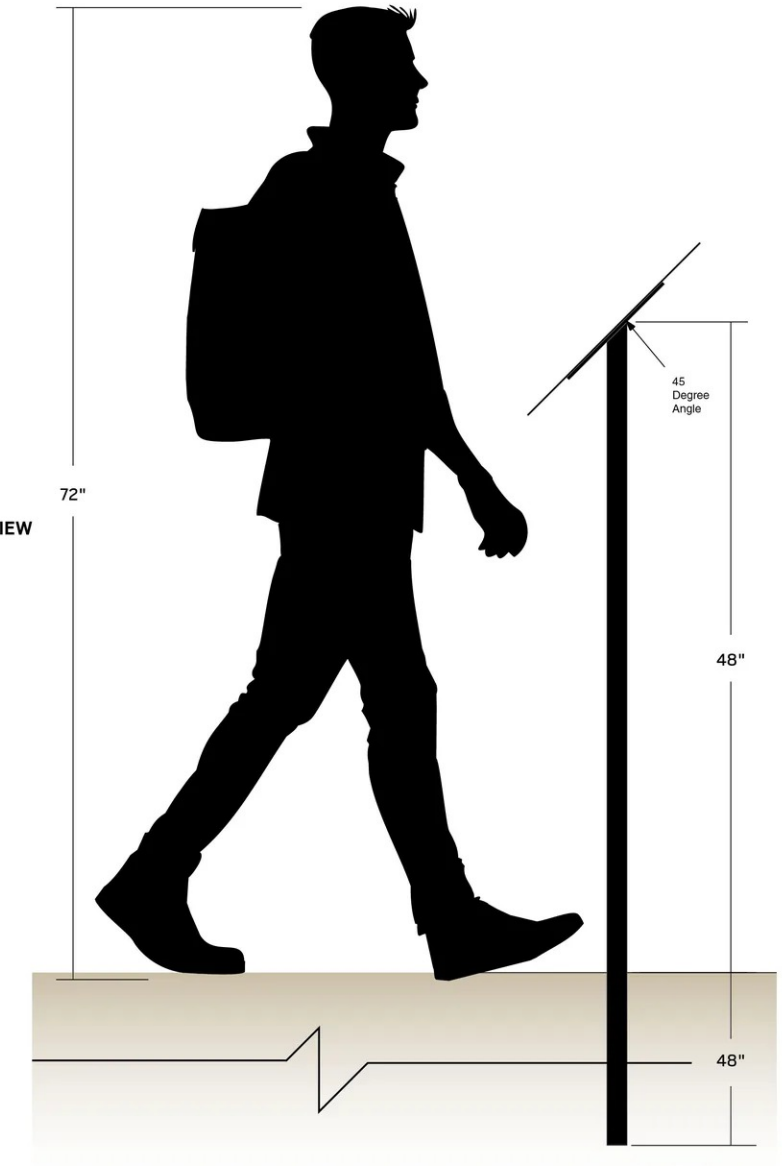

MOUNTING PLATE




SIDE VIEW




SIDE VIEW




SIDE VIEW
SCALE: 1:10

## SIGN TYPE: RAIN GARDEN SIGN
## SCALE: 1:5

☐ **MAXMETAL PANEL**
3MM THICK WHITE MAXMETAL PANEL WITH UV DIGITAL PRINT AND 8520 MATTE OVERLAMINATE
VHB TAPE MOUNTED TO MOUNTING PLATE
POST AND MOUNTING PLATE PAINTED BLACK
INK LAYERING: C

**MOUNTING**
- 1 1/2" DIAMETER GALVANIZED STEEL POST WITH MOUNTING PLATE AT 45 DEGREE ANGLE.
- MAXMETAL PANEL VHB TAPED TO MOUNTING PLATE.

**NOTES**

| | | | |
|---|---|---|---|
| **Project:** | Exterior Signage | **File Name:** | 30000_FEET_Rain_Garden_Sign R1.ai |
| **Client:** | 30000 Feet | **Origin Date:** | 07.10.25 |
| **Project Manager:** | J. Crawford | **Revised Date:** | 12.04.25 |
| **Drawn By:** | J. Raso | **Revision By:** | L. Weix |

**PLEASE EMAIL OR FAX YOUR APPROVAL BACK**

☐ **Approved As Is** ☐ **Approved With Changes** ☐ **Please Change and Resubmit**

X _____

This drawing is the sole property of SDDI Sign Systems. All rights to use and/or reproduce are reserved. Actual dimensions may vary slightly due to practical limitations with fabrication. Photographic representations of the proposed signage are for presentation only and may not be to scale. Colors will be printed as is, unless a specific color (i.e. Pantone Number, Sherwin Williams, or hard sample) is provided.

SDDI SIGNS
Define your image.
www.sddisigns.com
P. 952-224-9906 | F. 952-224-9909
17125 ADELMANN ST. SE
PRIOR LAKE, MN 55372